

ISLAMIC FACADE - CONNECTION AND CORNICE CORRECTION


Connected material joints, repaired profiles and new stepped Islamic roof crenellations.

PREVIOUS VERSION

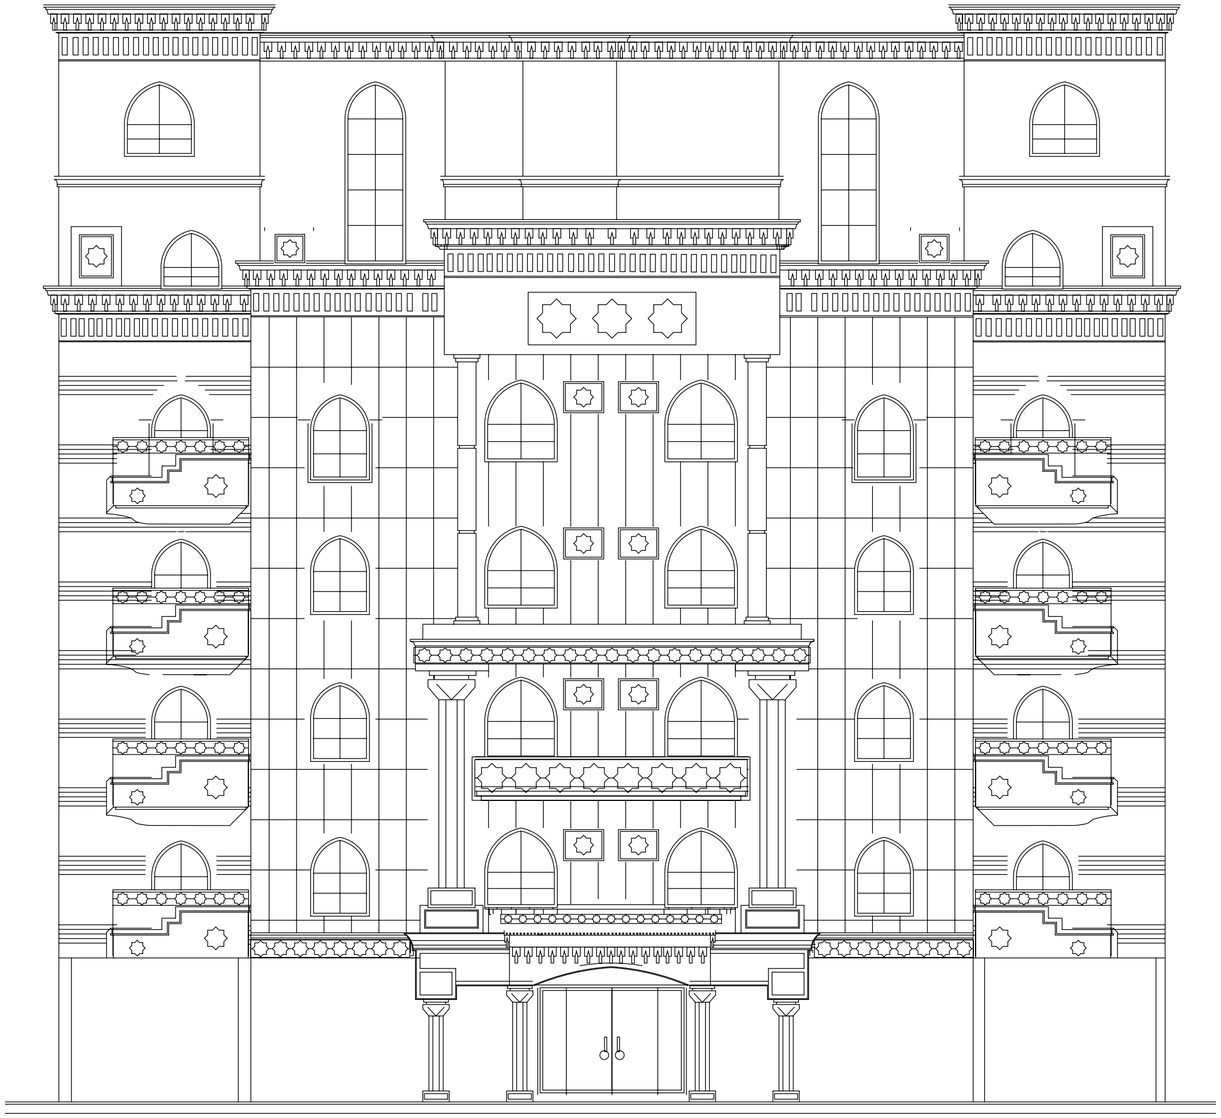


CORRECTED VERSION

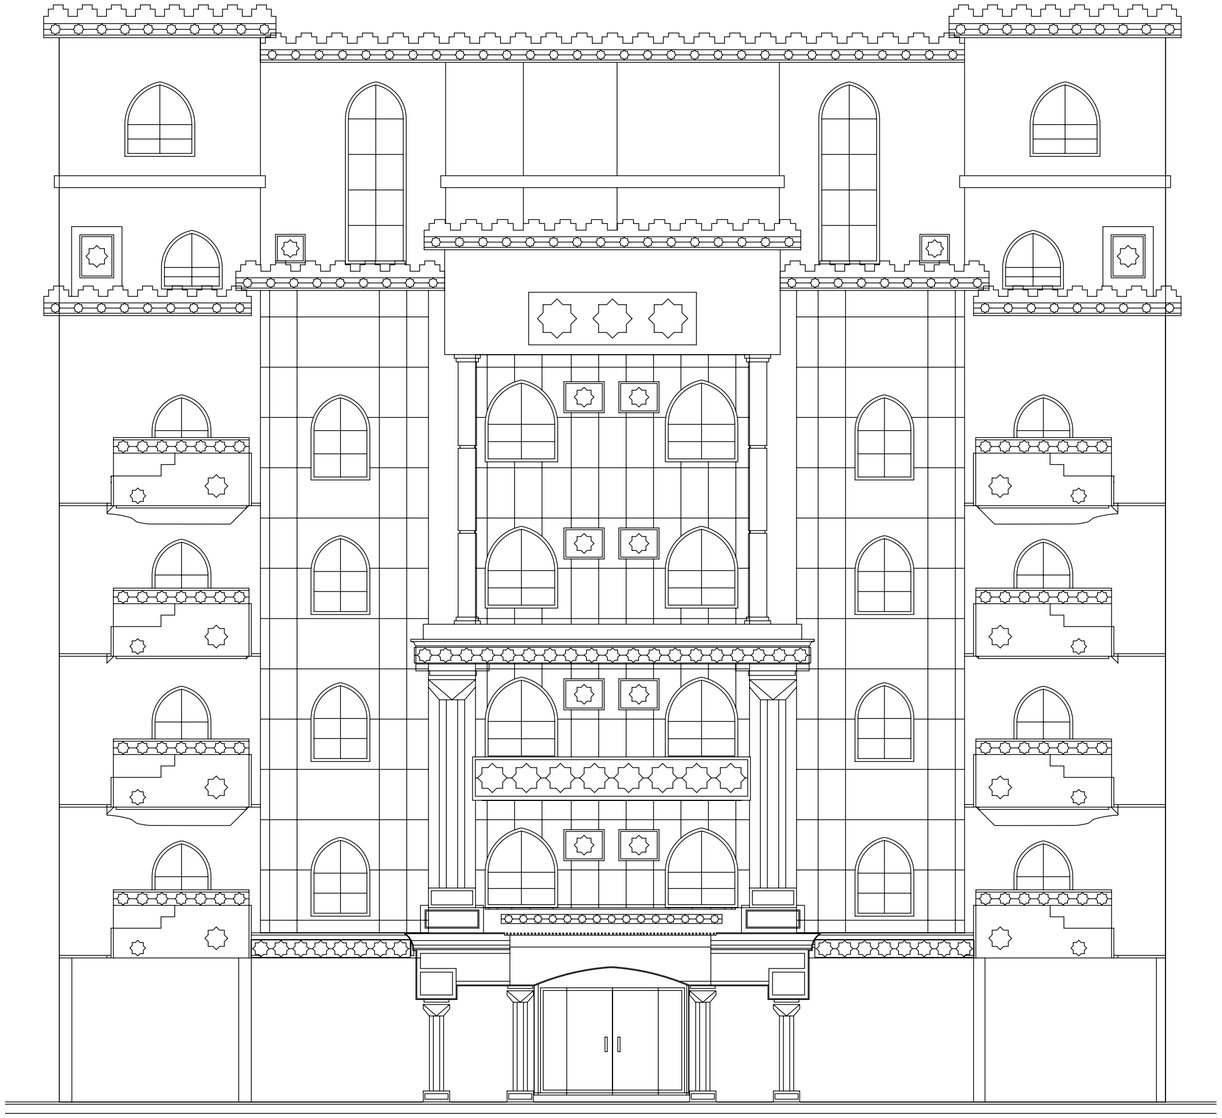

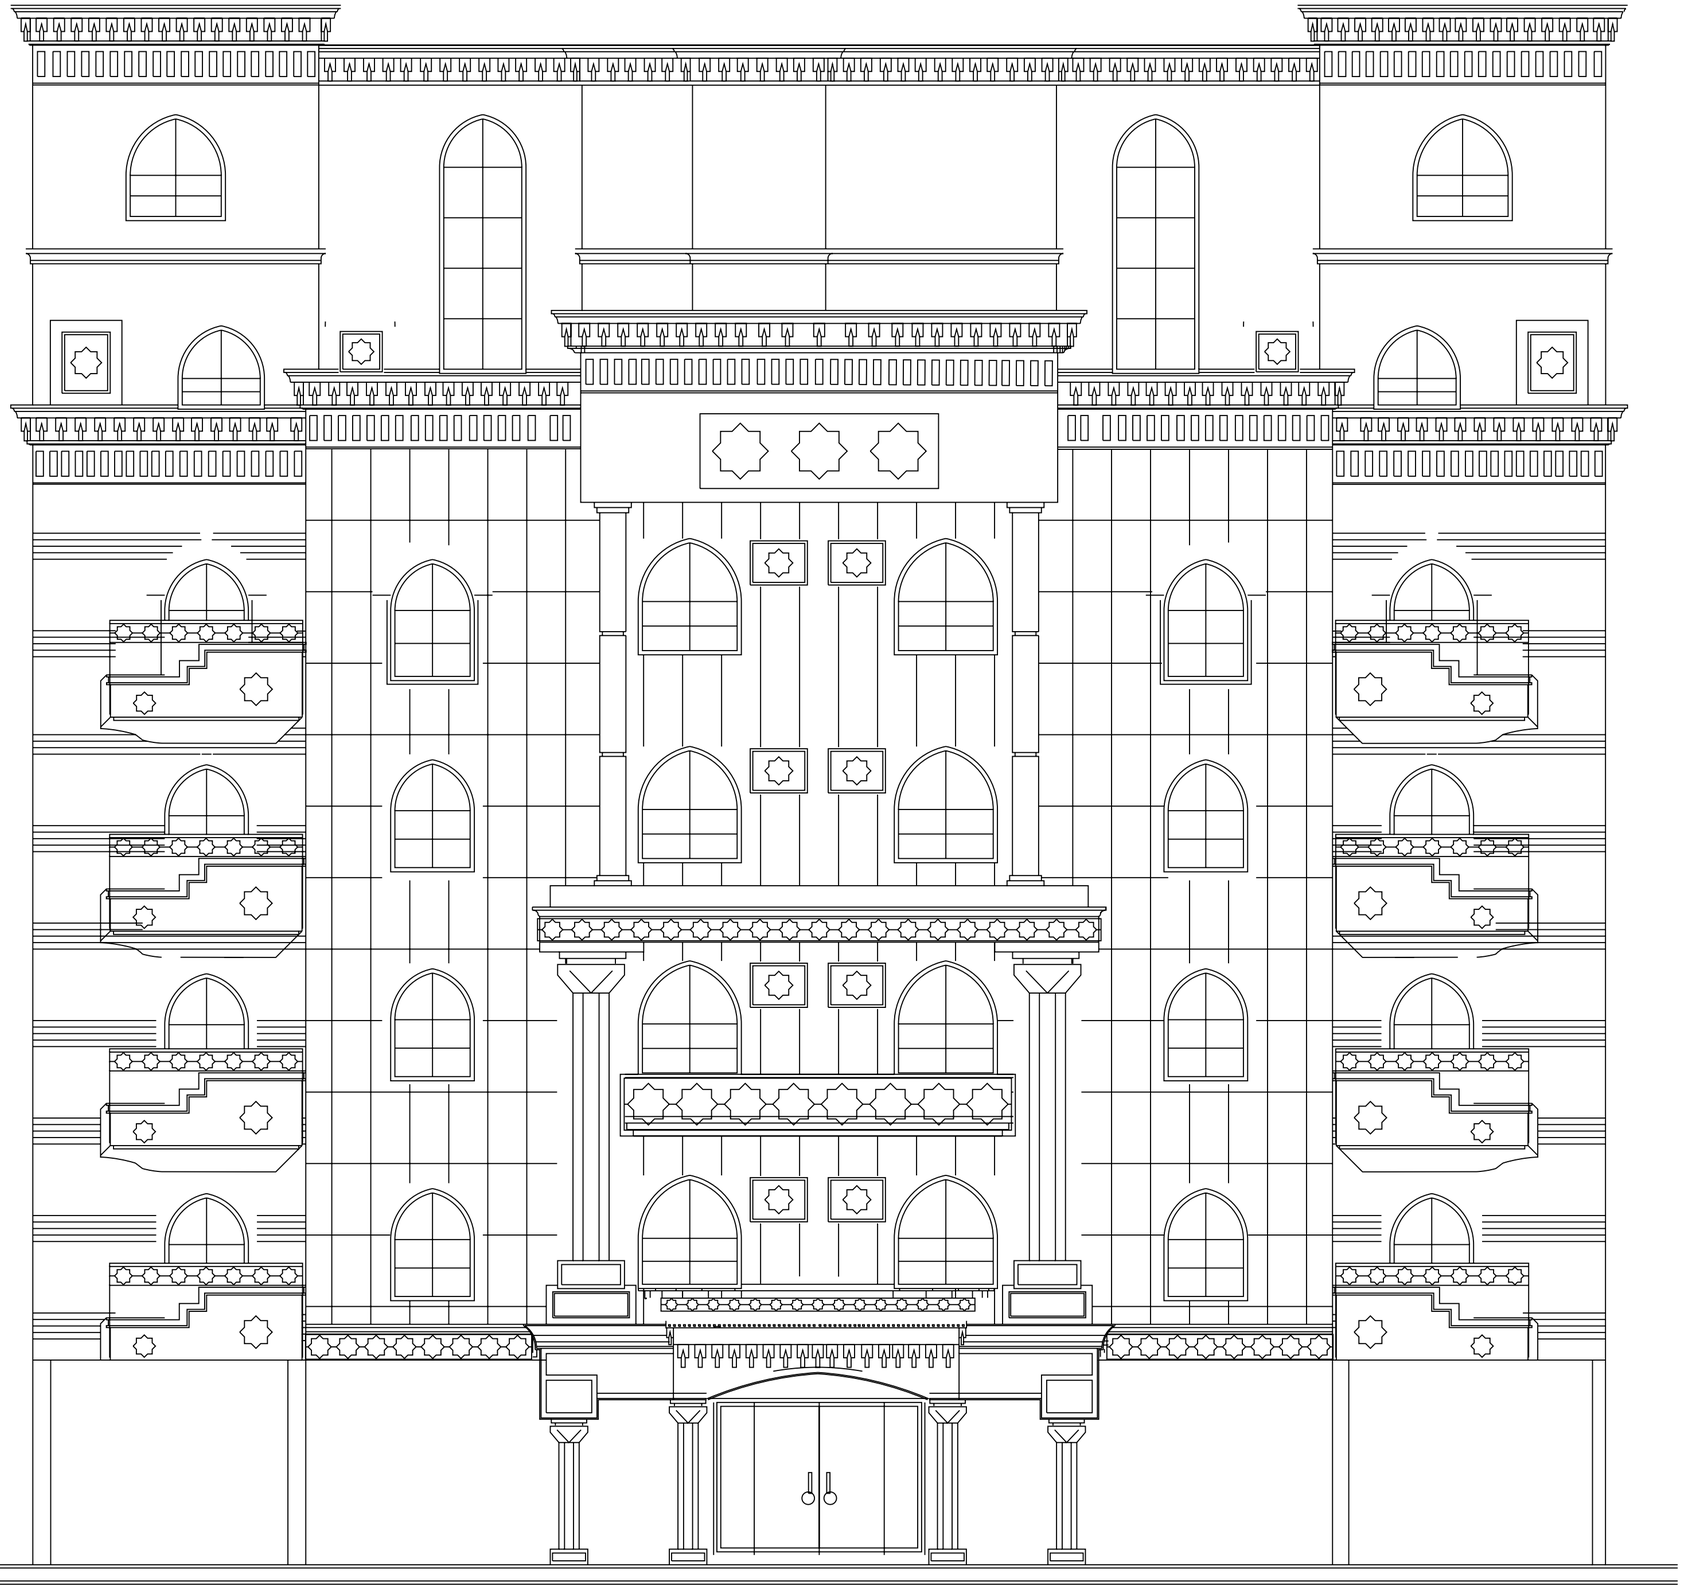

ISLAMIC ADAPTATION | ORIGINAL MASSING, BALCONY PROFILES AND CORNICE LEVELS

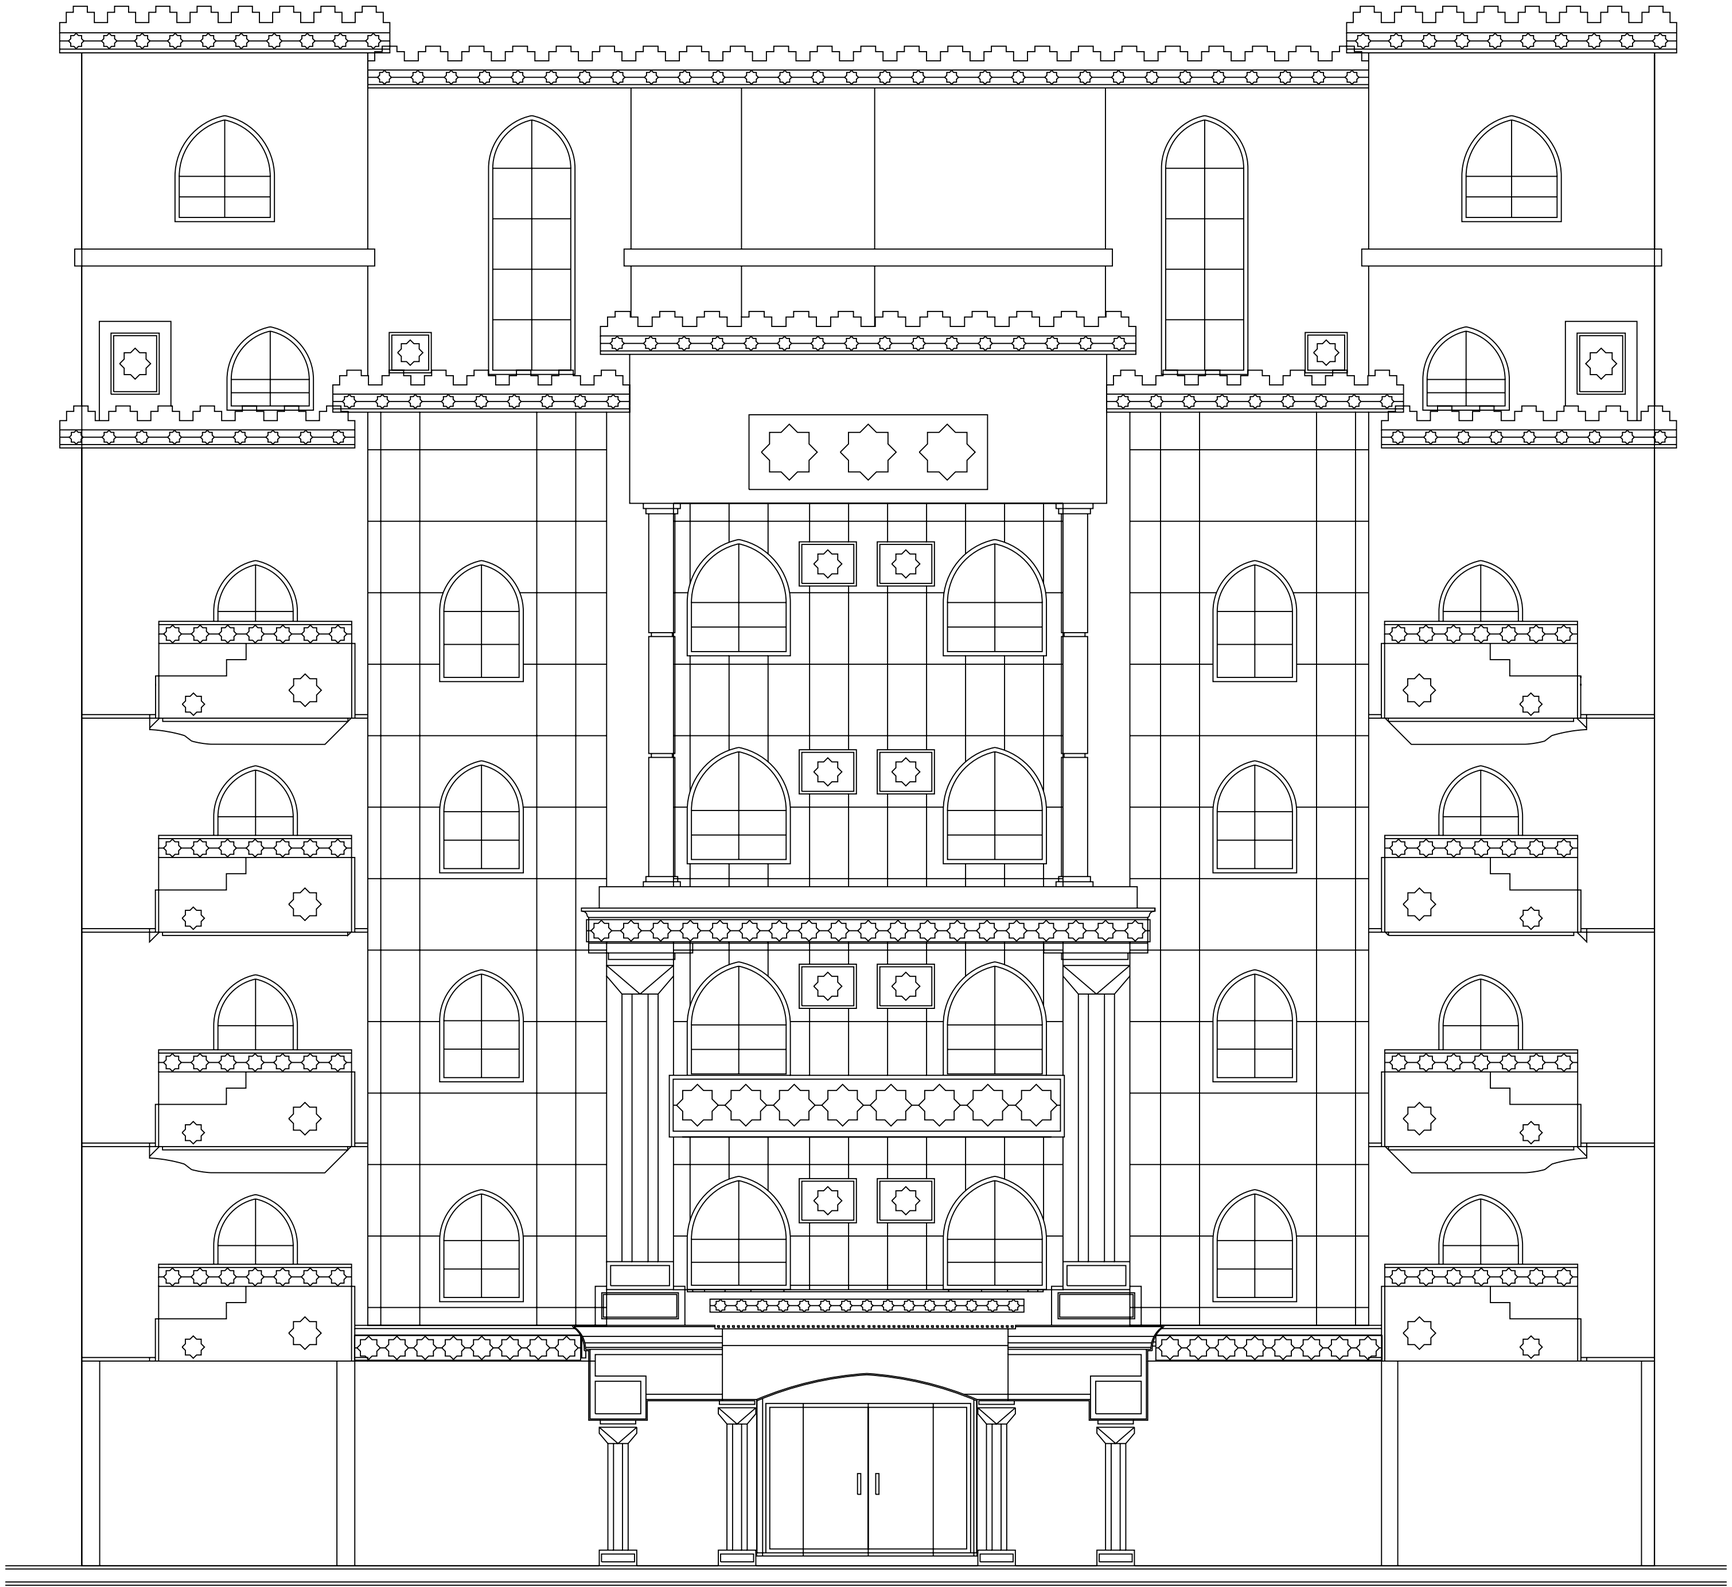

ISLAMIC FACADE V2 | CONNECTED LINEWORK / STEPPED ISLAMIC CRENELLATIONS