

اتجاهات جديدة لتغيير تصميم الواجهة

معاينات تصورية للمقارنة واختيار الطراز

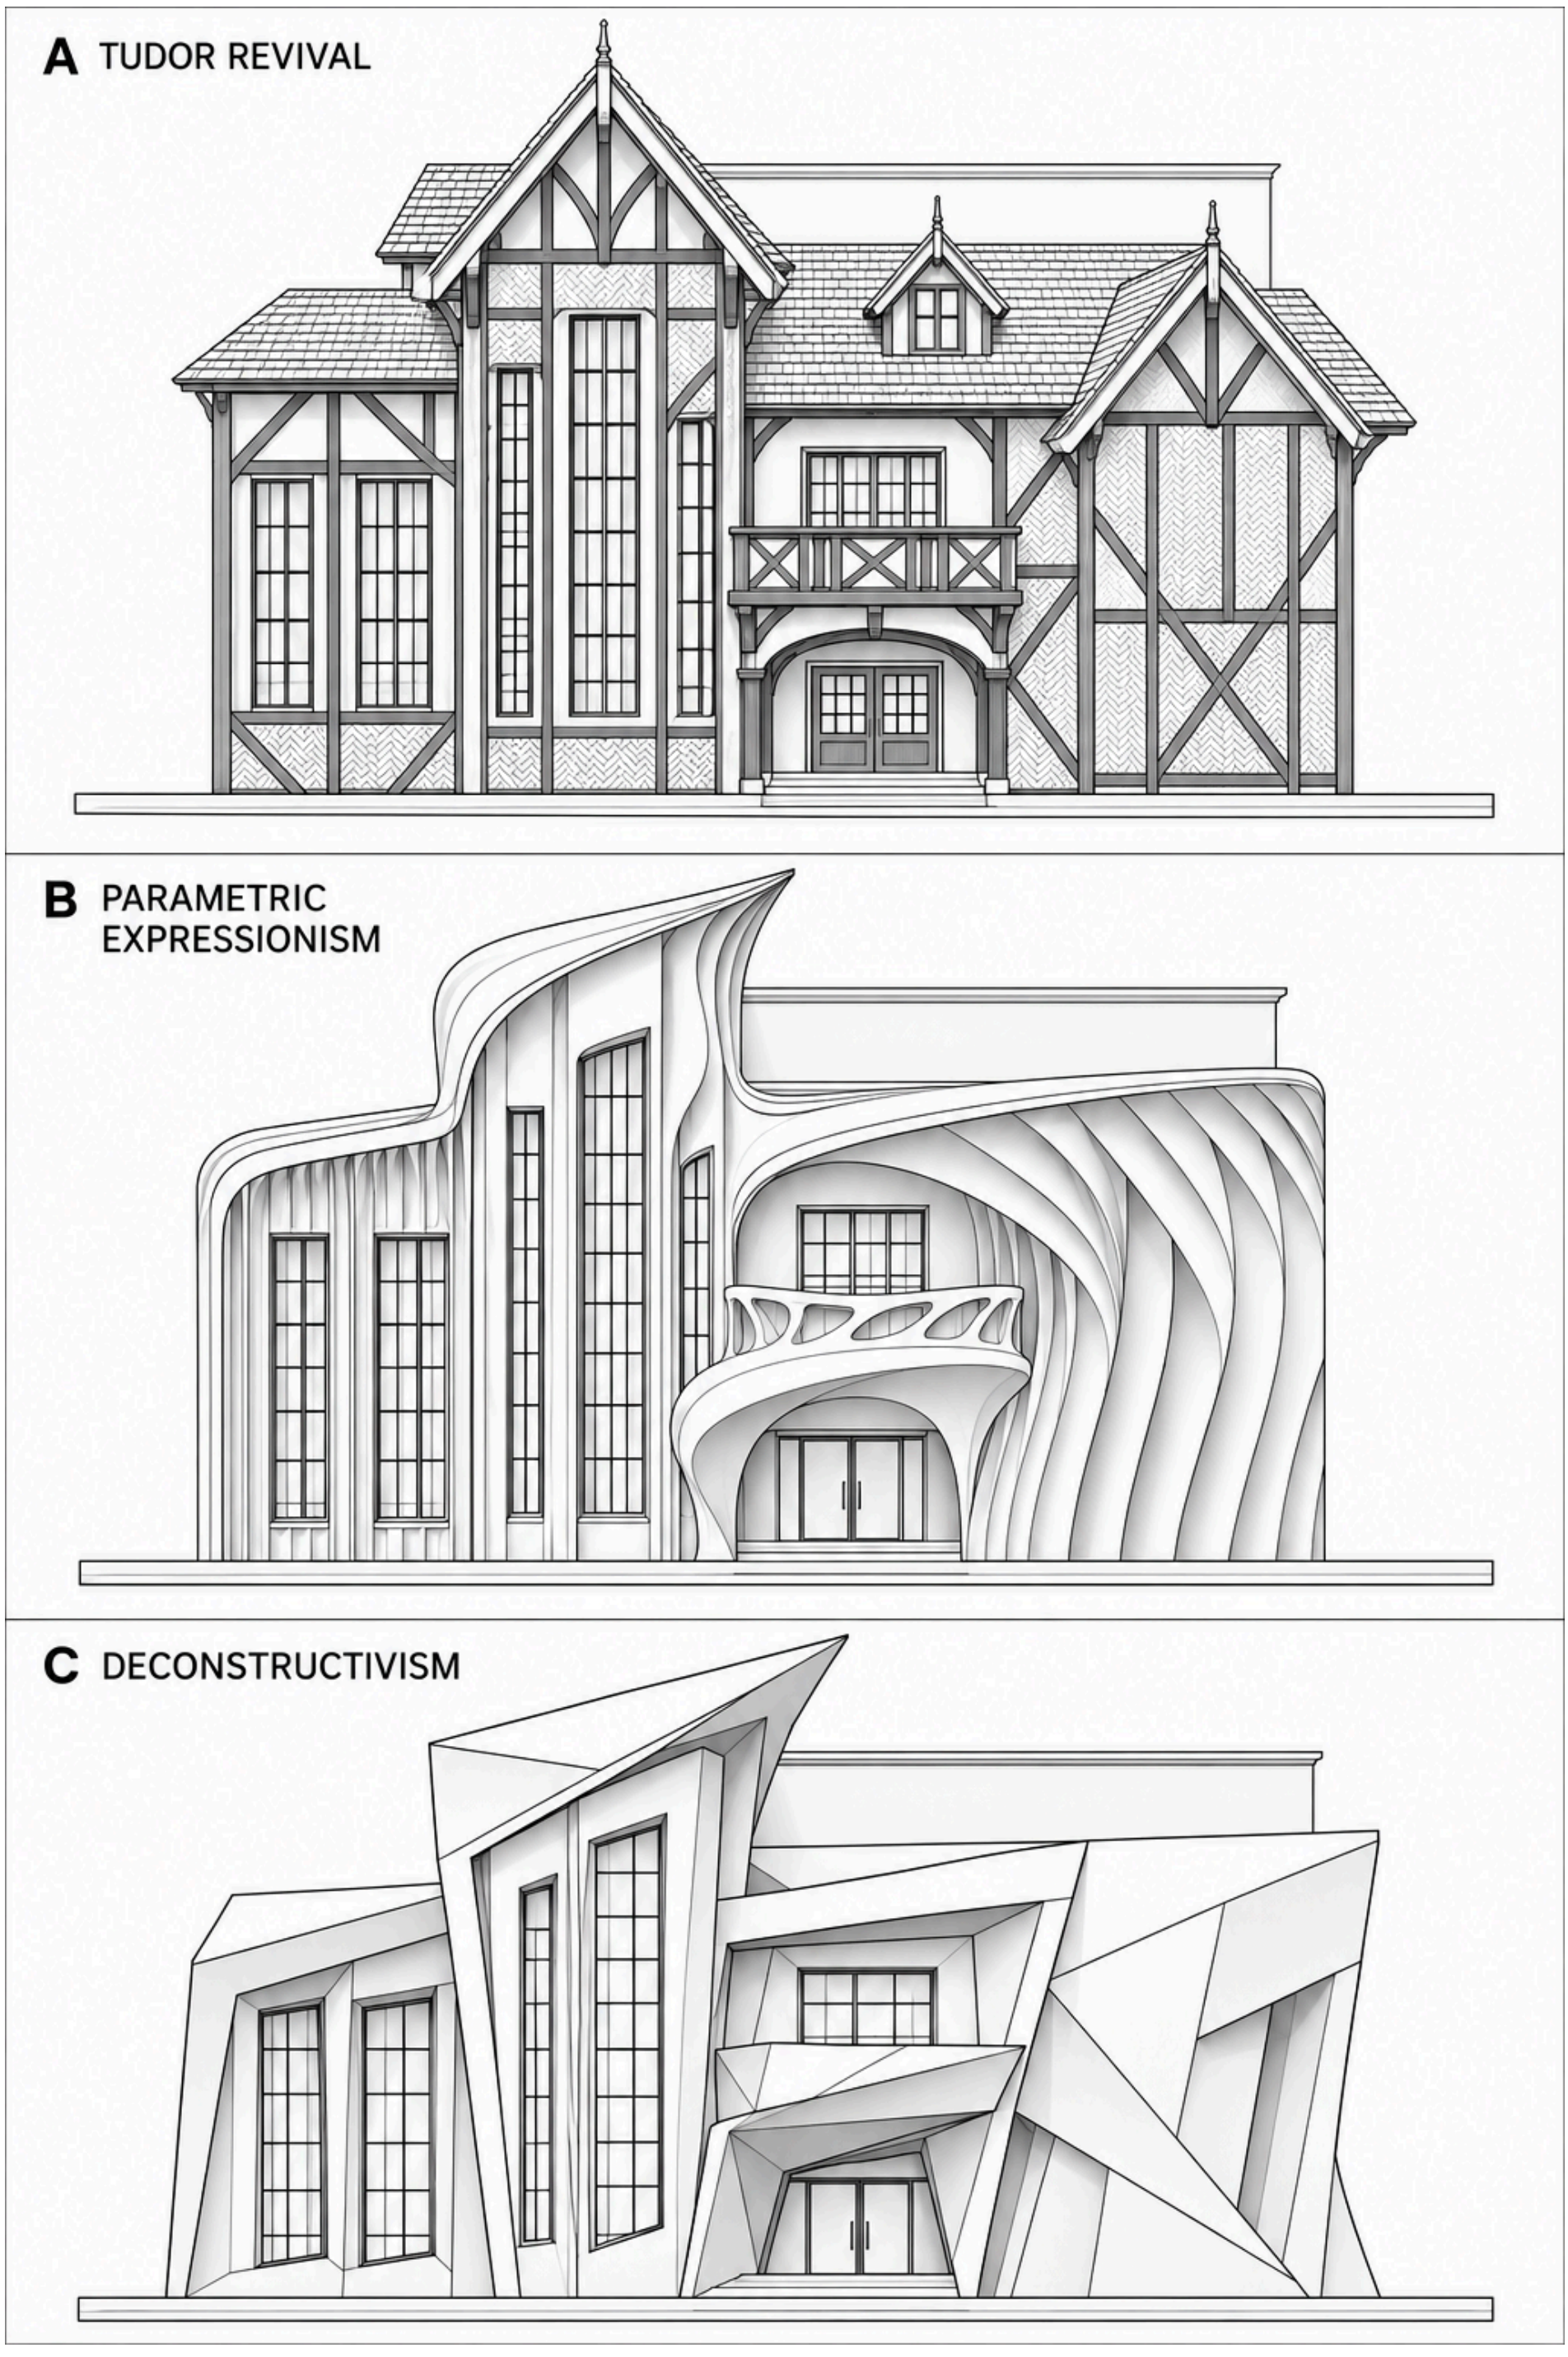

دراسة شكلية أولية؛ ضبط الأبعاد والتفاصيل الهندسية بعد اختيار الاتجاه.


A: تيودور إحيائي

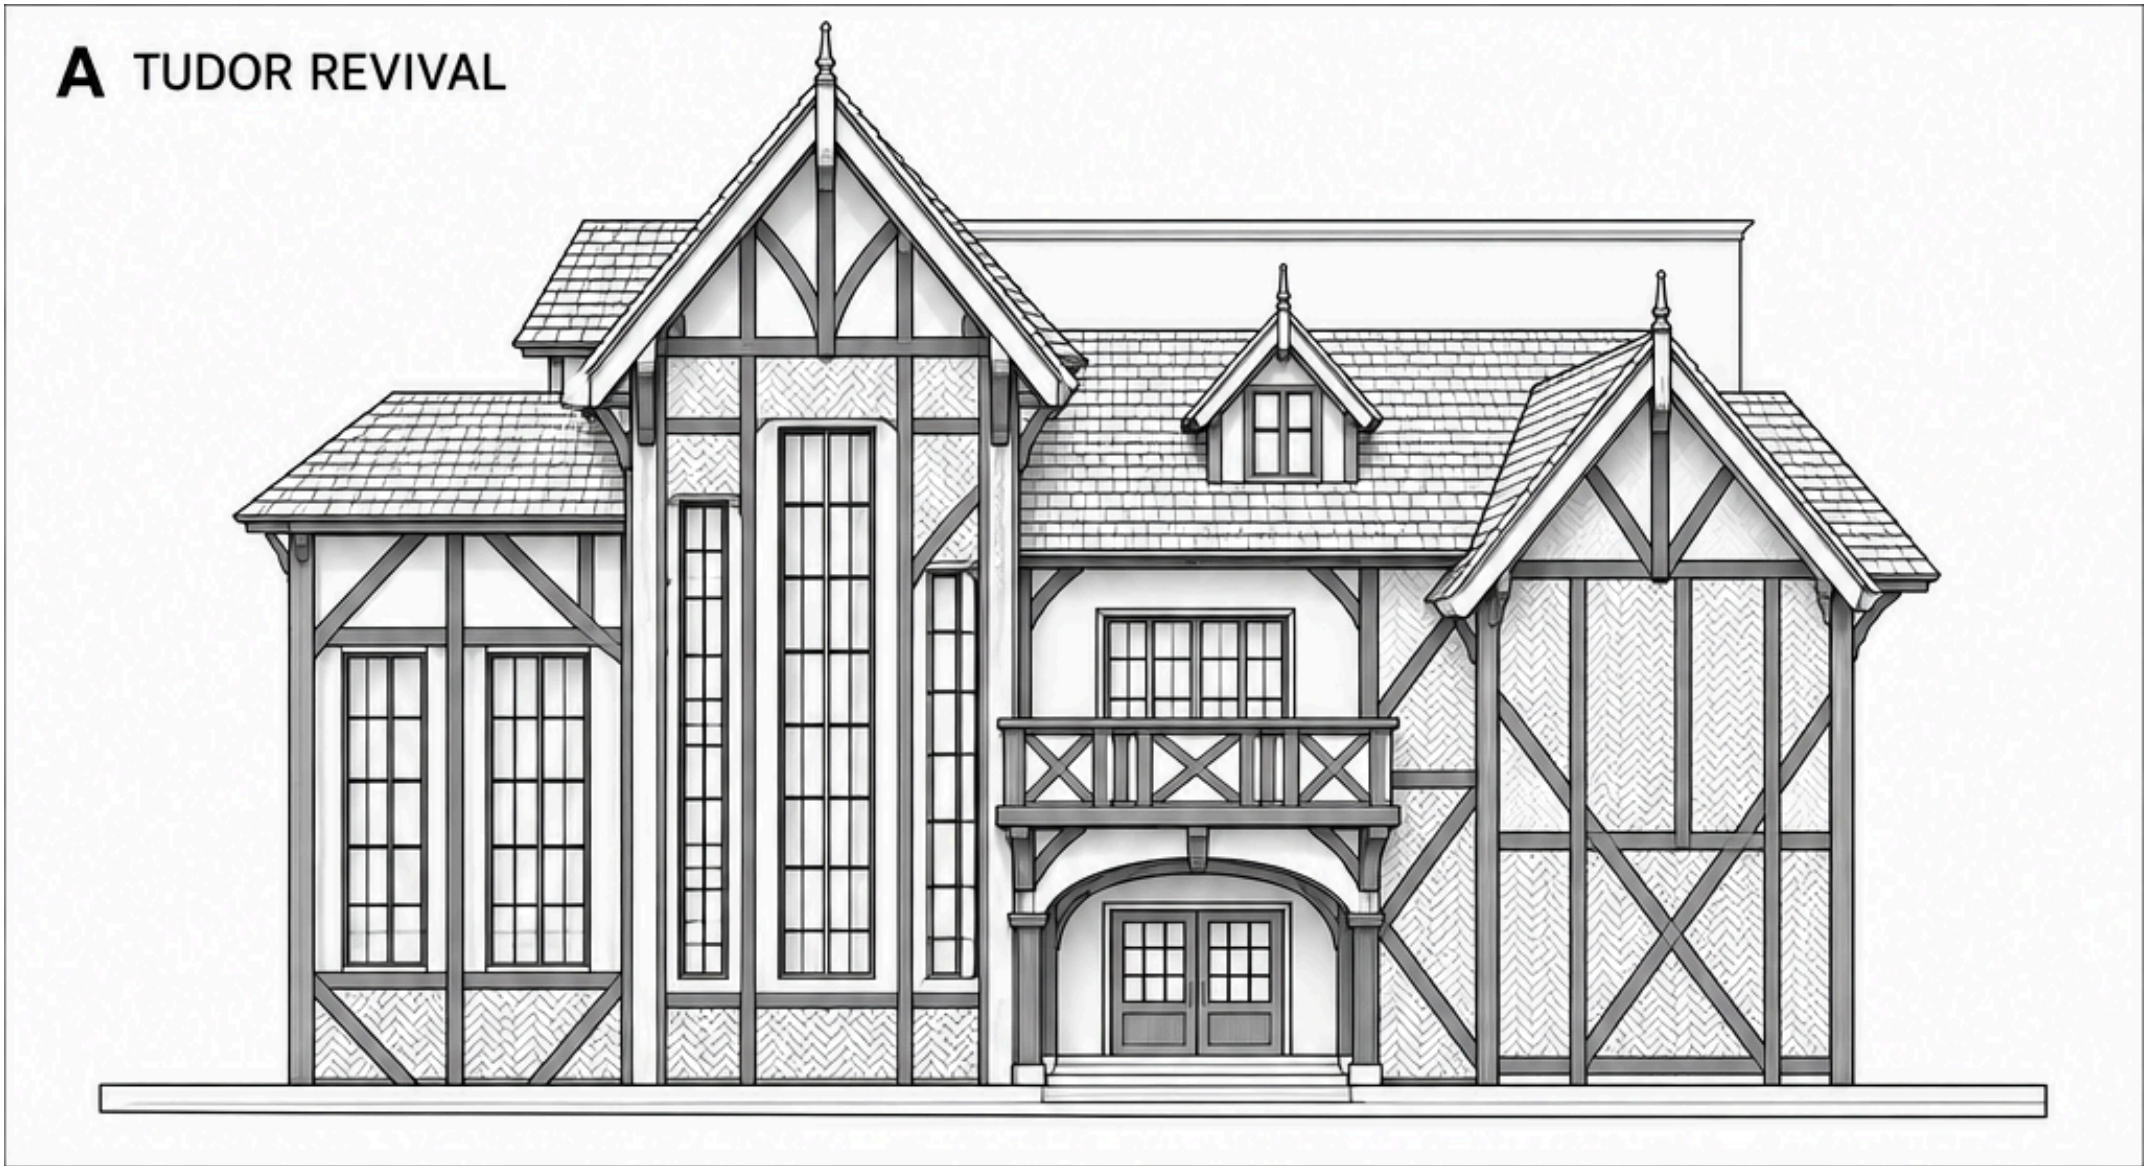

تكوين بأسقف جملونية بارزة، وعناصر مائلة ومتقاطعة، وبلكونة ذات إطار وتفاصيل مختلفة.

معاينة تصورية للاختيار؛ توزيع الفتحات والتفاصيل هنا مبدئي.

B: تعبيري بارامتري

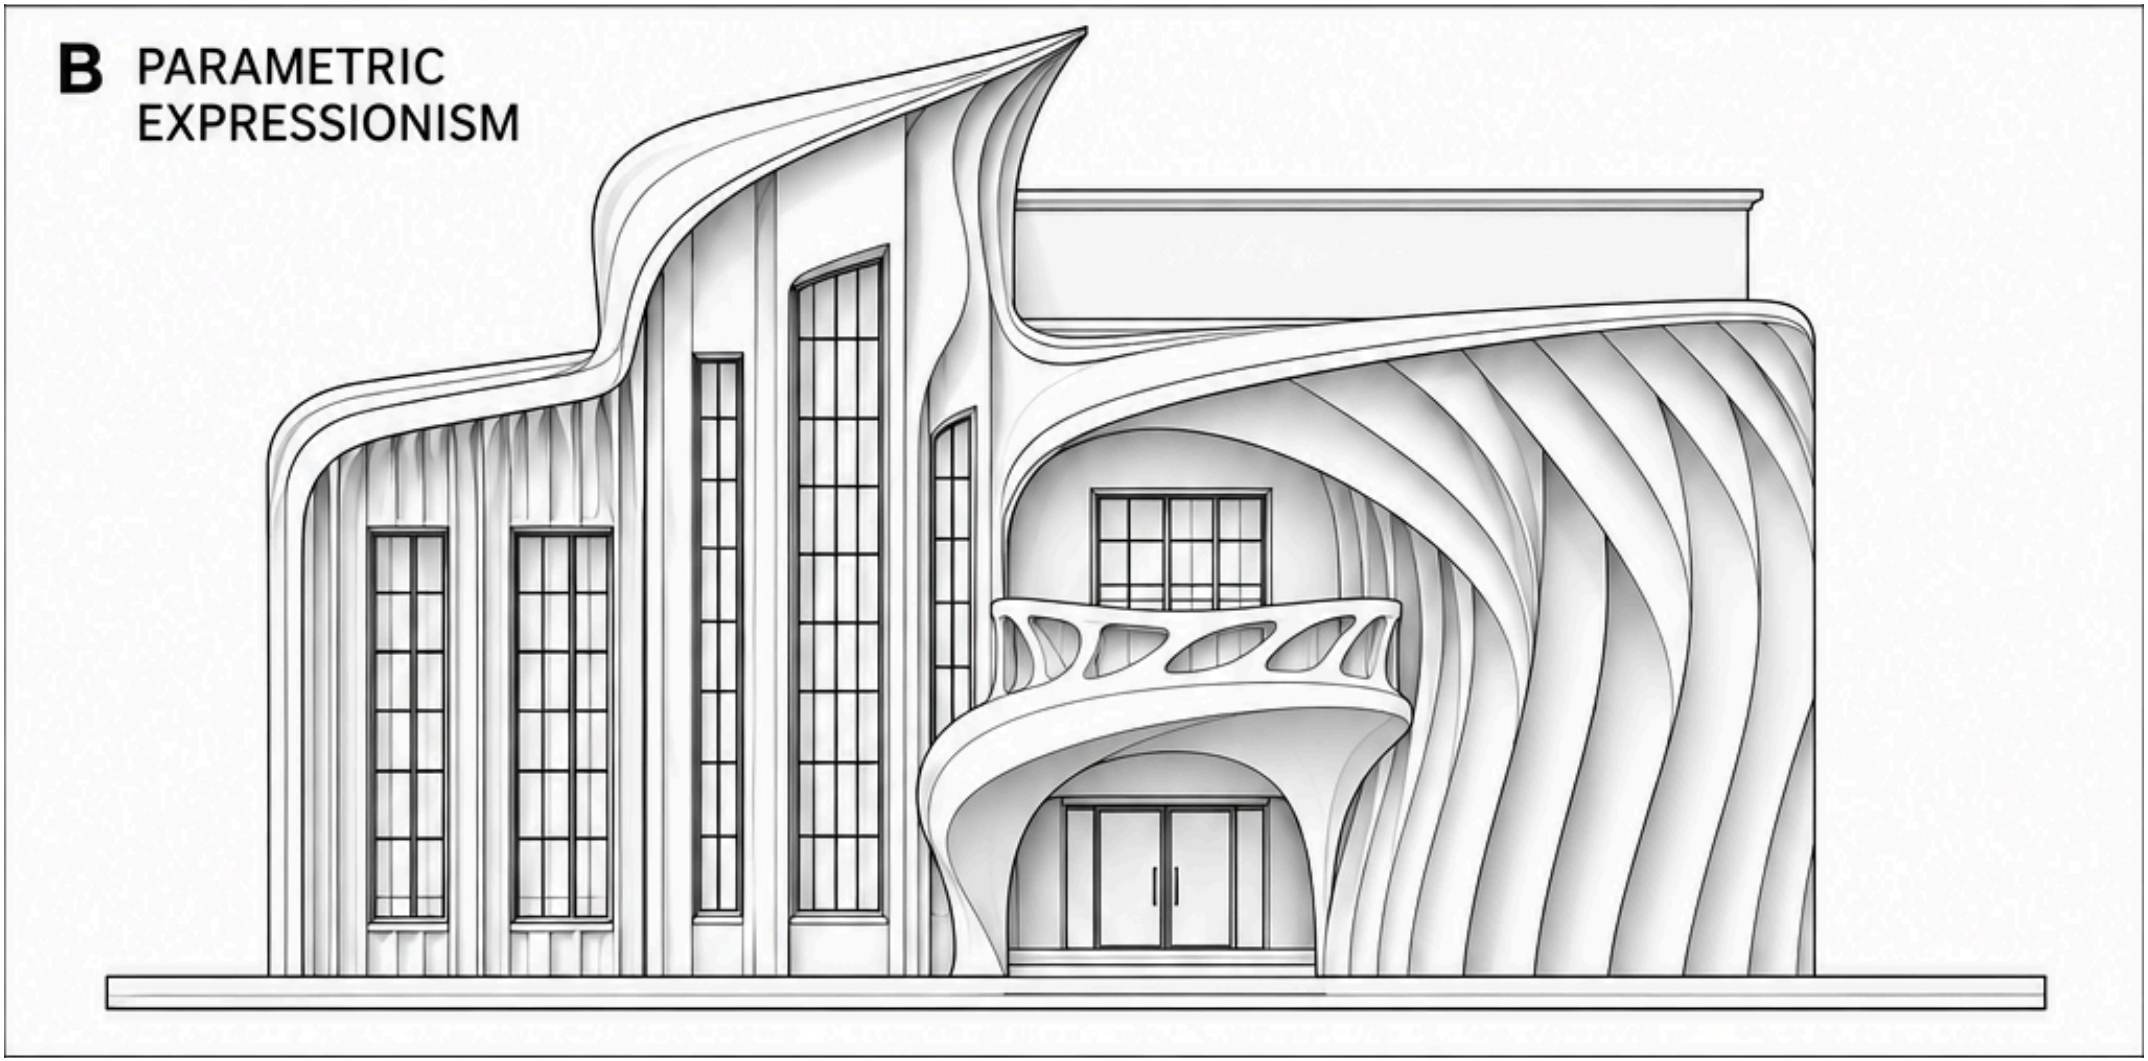

شرائط وانحناءات تربط البرج بالمدخل والجناح اليمين، مع نهاية جديدة للبرج ومعالجة متدرجة للكتلة المصمتة.

معاينة تصورية للاختيار؛ توزيع الفتحات والتفاصيل هنا مبدئي.

C: تفكيكي



أسطح مطوية وزوايا مائلة، ومدخل وبلكونة بتكوين زاوي، ونهاية حادة وغير متماثلة للبرج.

معاينة تصورية للاختيار؛ توزيع الفتحات والتفاصيل هنا مبدئي.