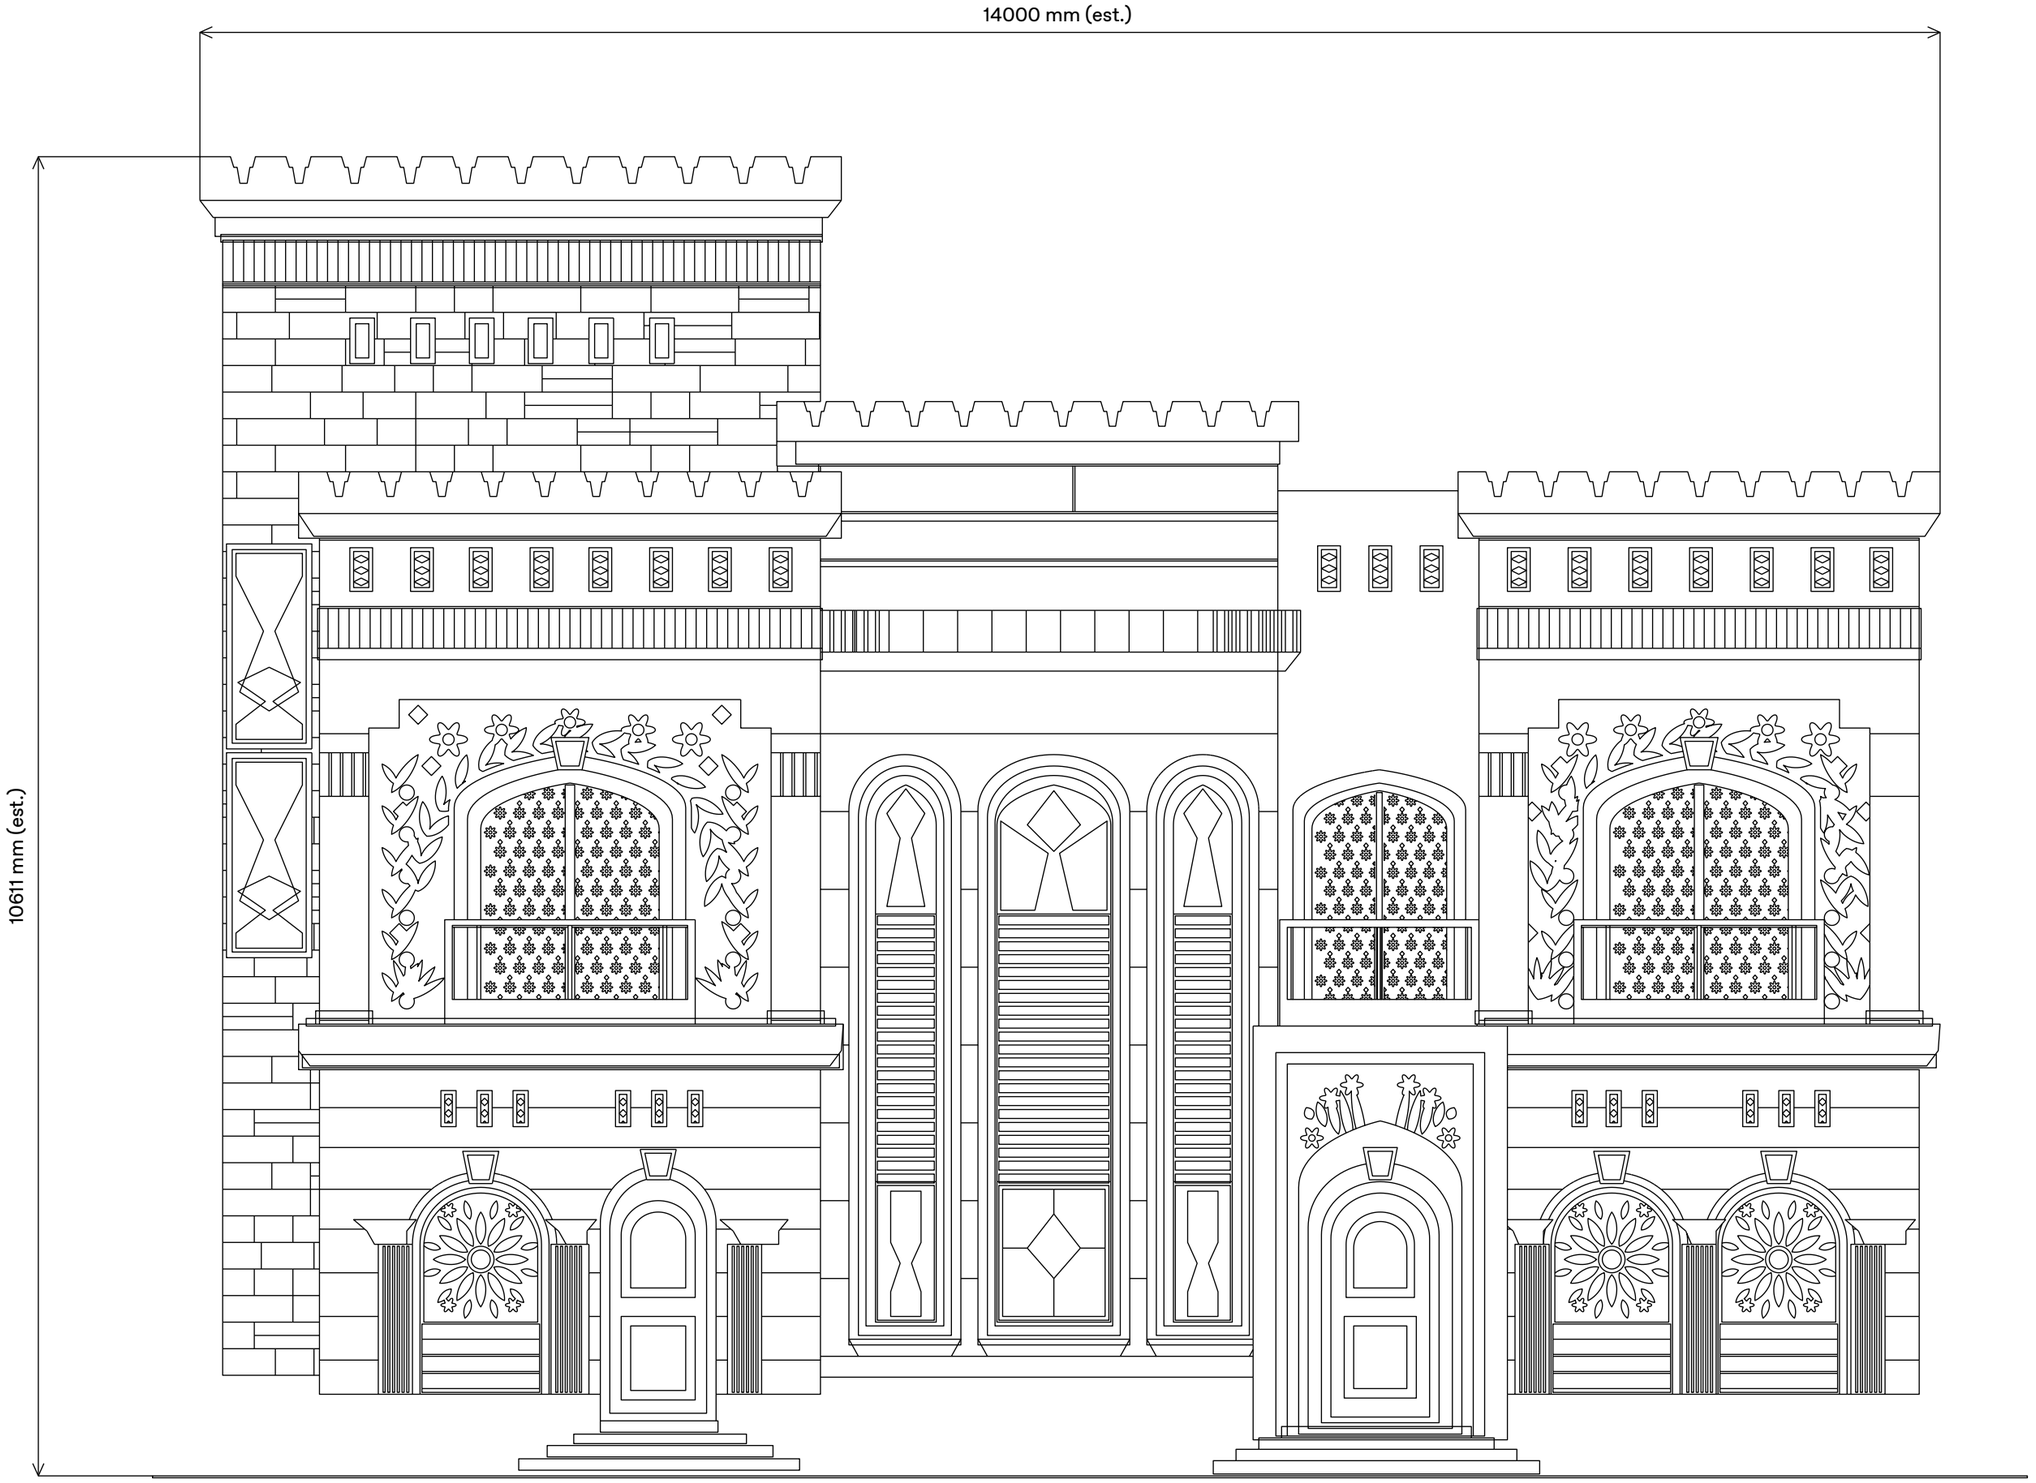


ESTIMATED GEOMETRY - 14,000 mm nominal width - black 0.18 mm - dimensions are not surveyed

ESTIMATED DIMENSION SCHEDULE (mm)

Visual reconstruction. All values are proportional estimates, not construction measurements.

ID / ELEMENT	WIDTH (mm)	HEIGHT / LEVEL (mm)
OVERALL_WIDTH - Overall facade width	14000	-
TOWER_HEIGHT - Highest crown above ground datum	-	10611
MIDDLE_CROWN - Middle crown above ground datum	-	8641
SIDE_CROWNS - Side crowns above ground datum	-	8076
BELT_CORNICE - Lower edge of first-floor belt above datum	-	3298
LEFT_DOOR - Left door opening	931	2046
CENTRAL_DOOR - Projecting entrance door	947	1939
LEFT_BALCONY - Left upper opening	1863	2000
RIGHT_BALCONY - Right upper opening	1863	2000
RECESS_OPENING - Recessed upper opening	1389	1893
NARROW_TALL_WINDOWS - Narrow tall outer frames	901	4748
MIDDLE_TALL_WINDOW - Middle tall outer frame	1221	4748
GROUND_ROSE_WINDOWS - Outer rose-window frames	1221	1786
LEFT_WING - Left front-wing width	4031	-
RIGHT_WING - Right front-wing width	3542	-
CENTRAL_BAY - Central bay width	3679	-

AutoLISP: APPLOAD palace_facade_clean.lsp, then type PALACE.

Pick an insertion point; accept 14000 mm or enter a different total width. PALACEDIMS adds native dimensions.

Geometry is shared with the DXF and the embedded AutoLISP data. No external image or CAD import is required.