


CONTEMPORARY ISLAMIC TRANSFORMATION | SIMPLE ARCHES / SPARSE ORNAMENT

BEFORE | SUPPLIED CLASSICAL FACADE

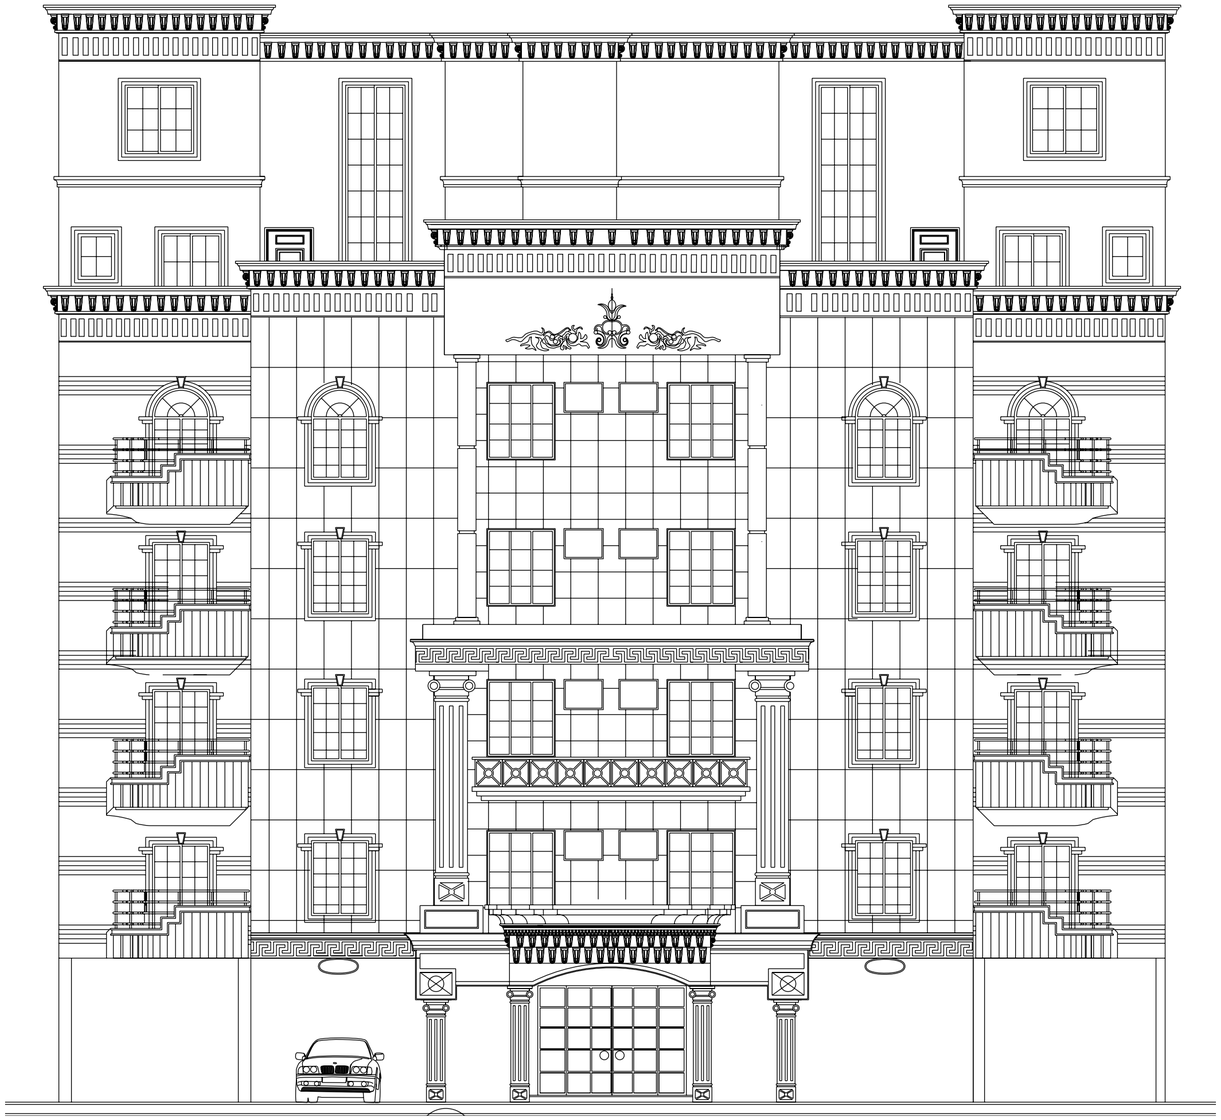


AFTER | CONTEMPORARY ISLAMIC

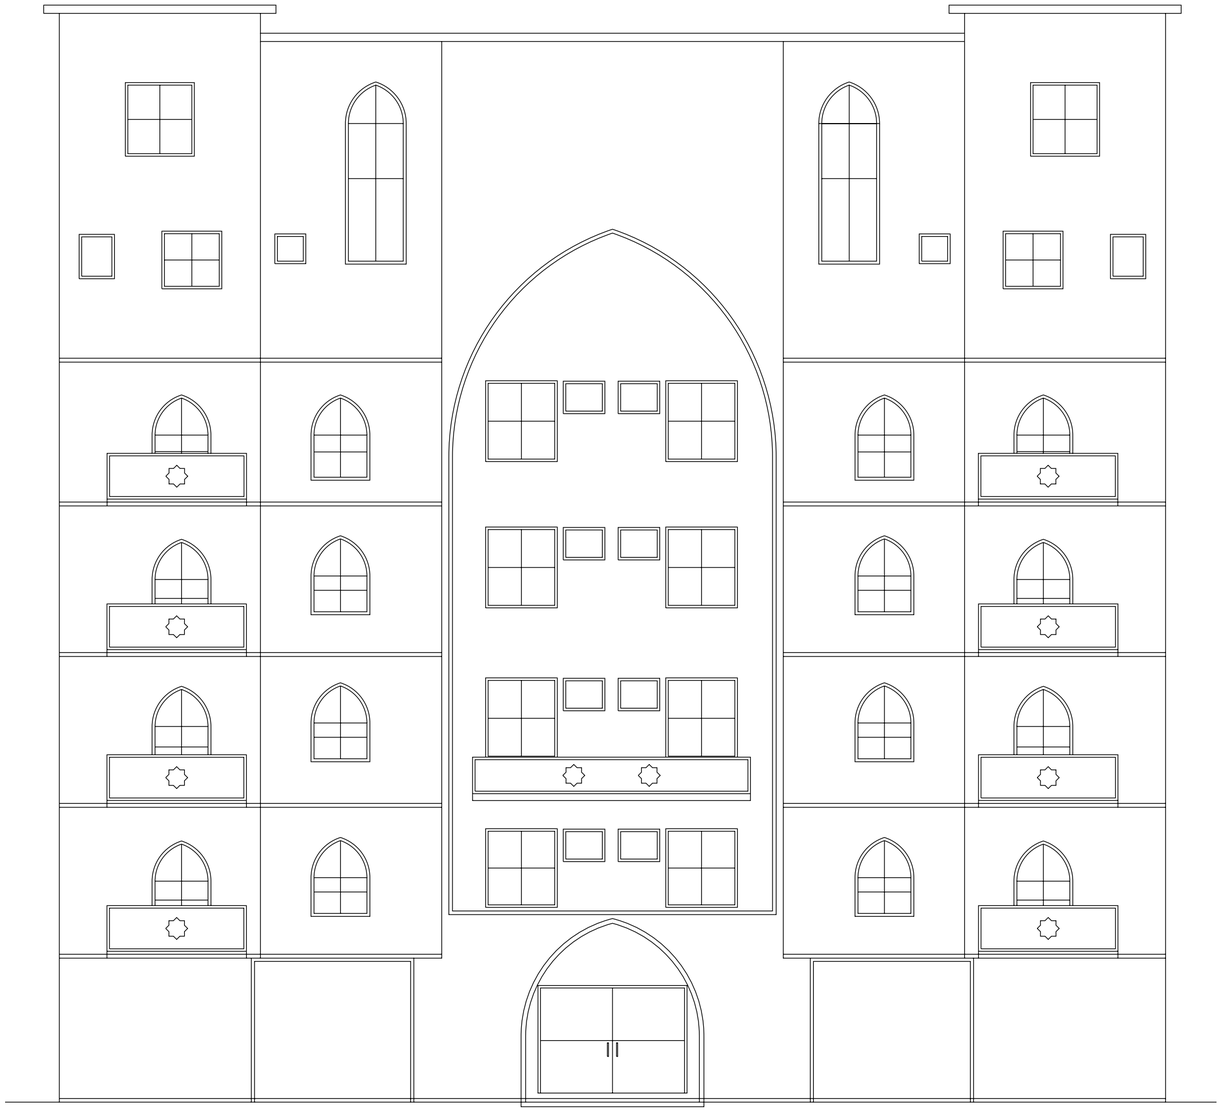

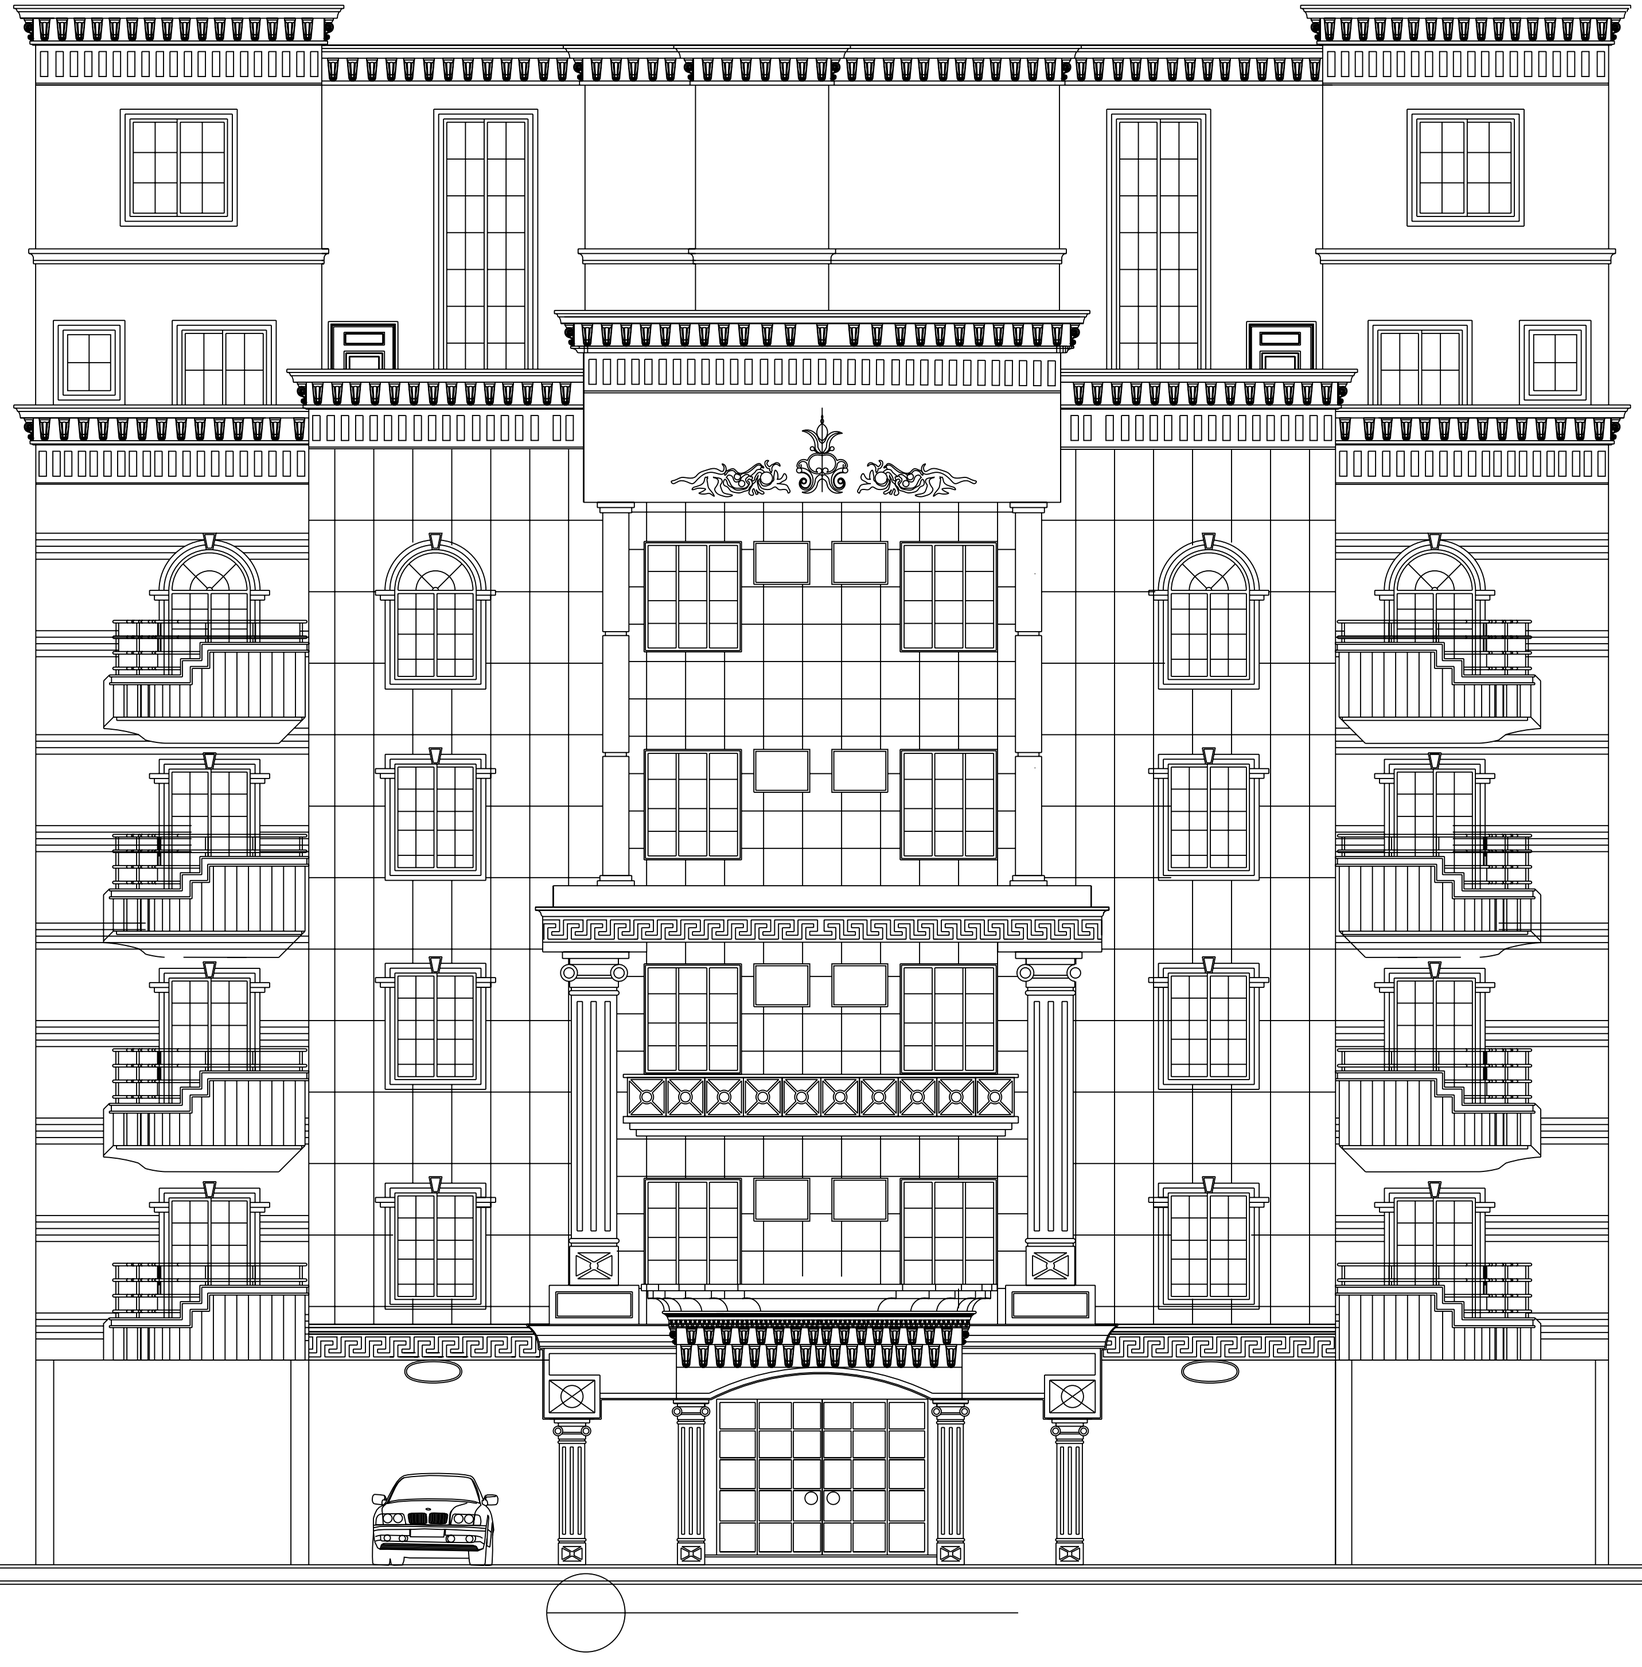

ORIGINAL FACADE | NATIVE GEOMETRY

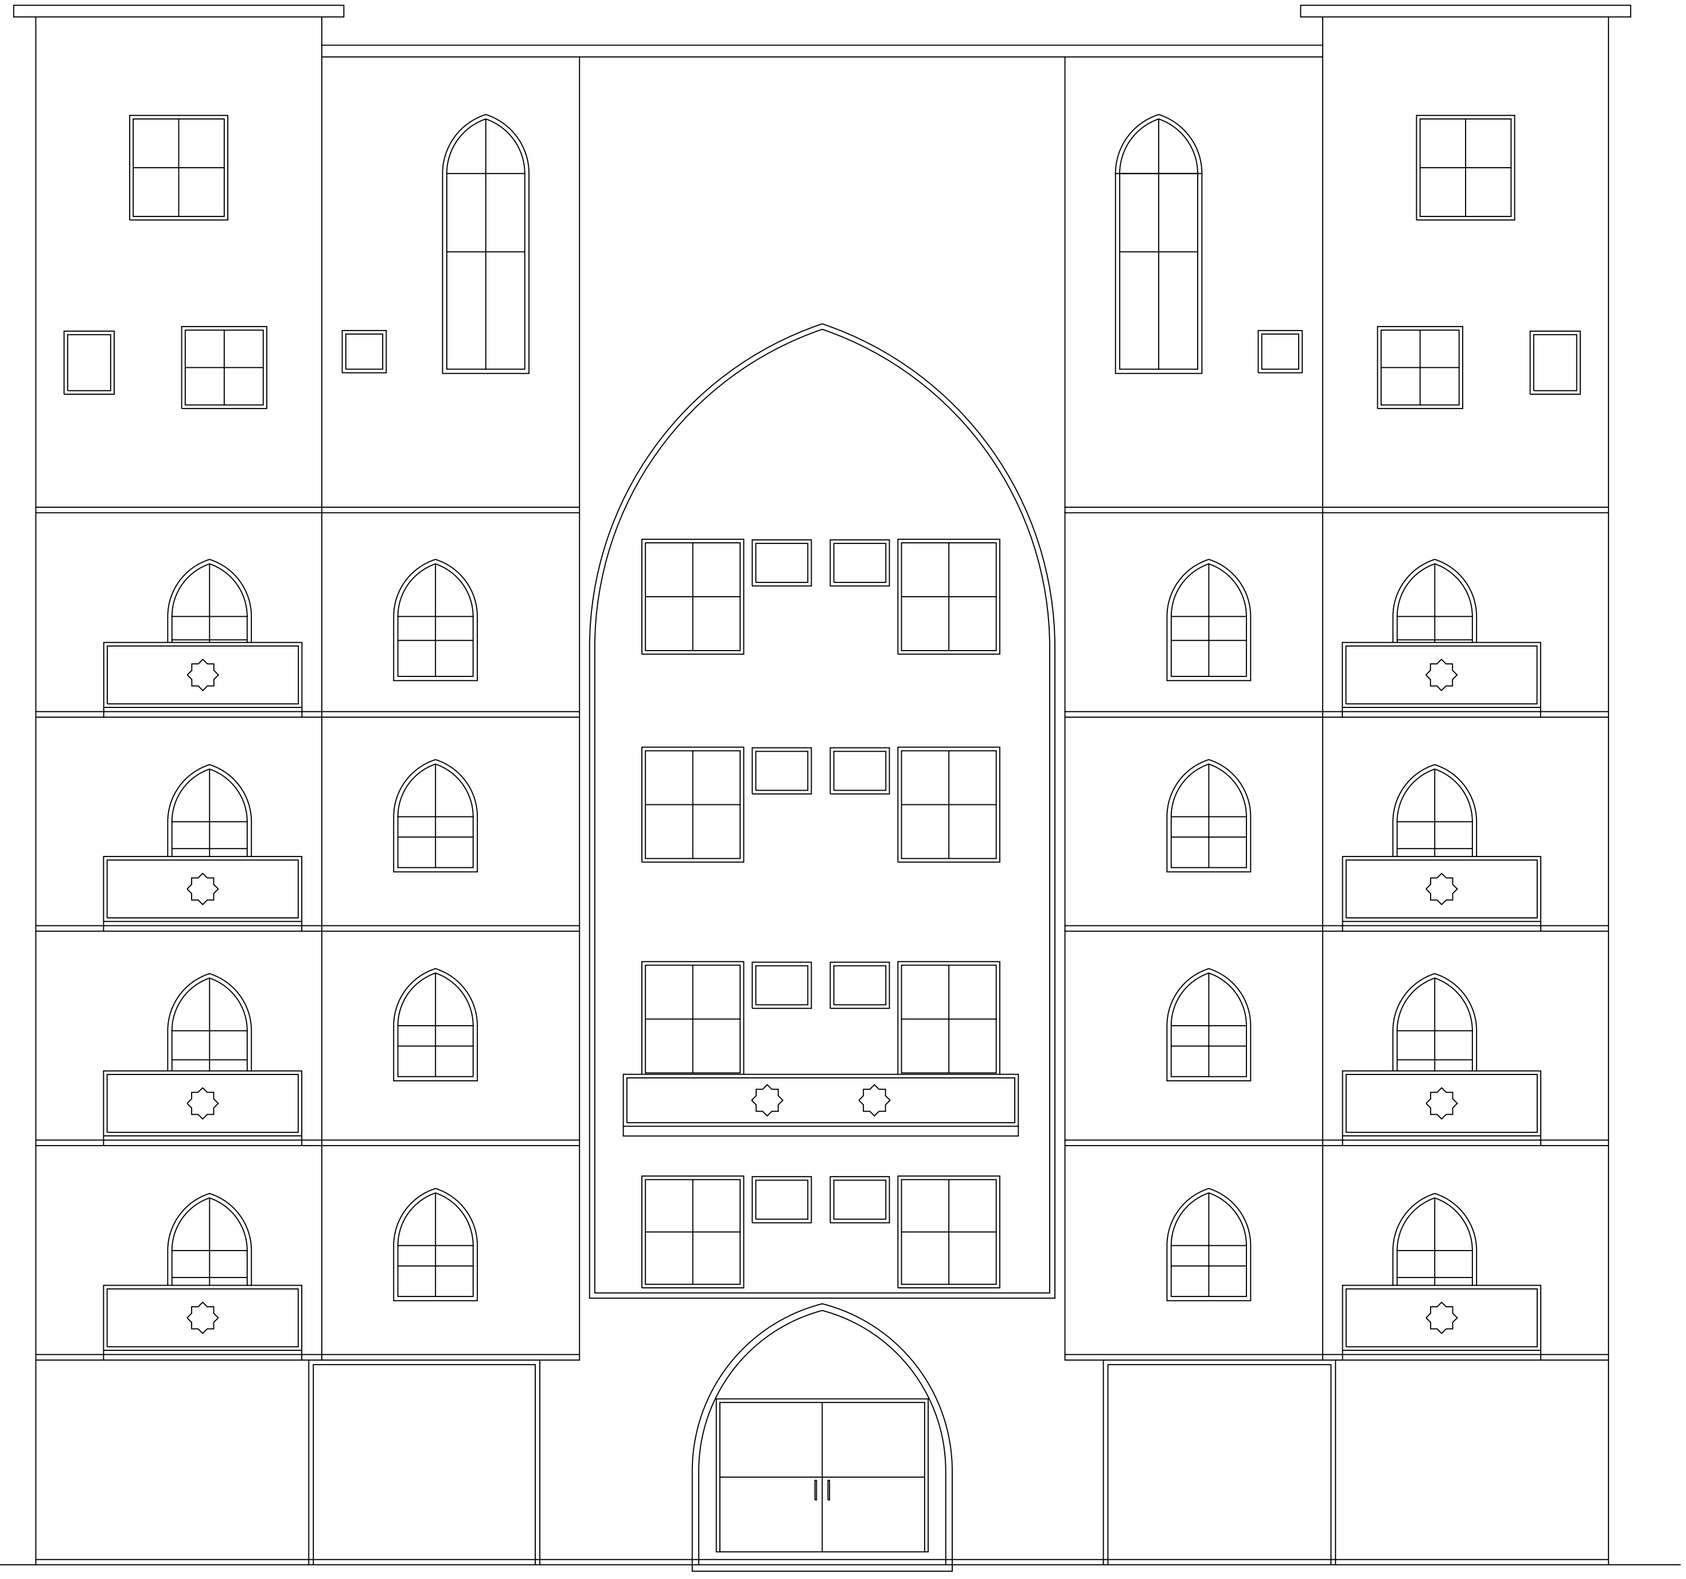

CONTEMPORARY ISLAMIC FACADE | SIMPLE POINTED ARCHES / SPARSE GEOMETRY / NO PLANTING