

CENTRAL BAY: ORIGINAL / ARCHITECTURE RESTORED

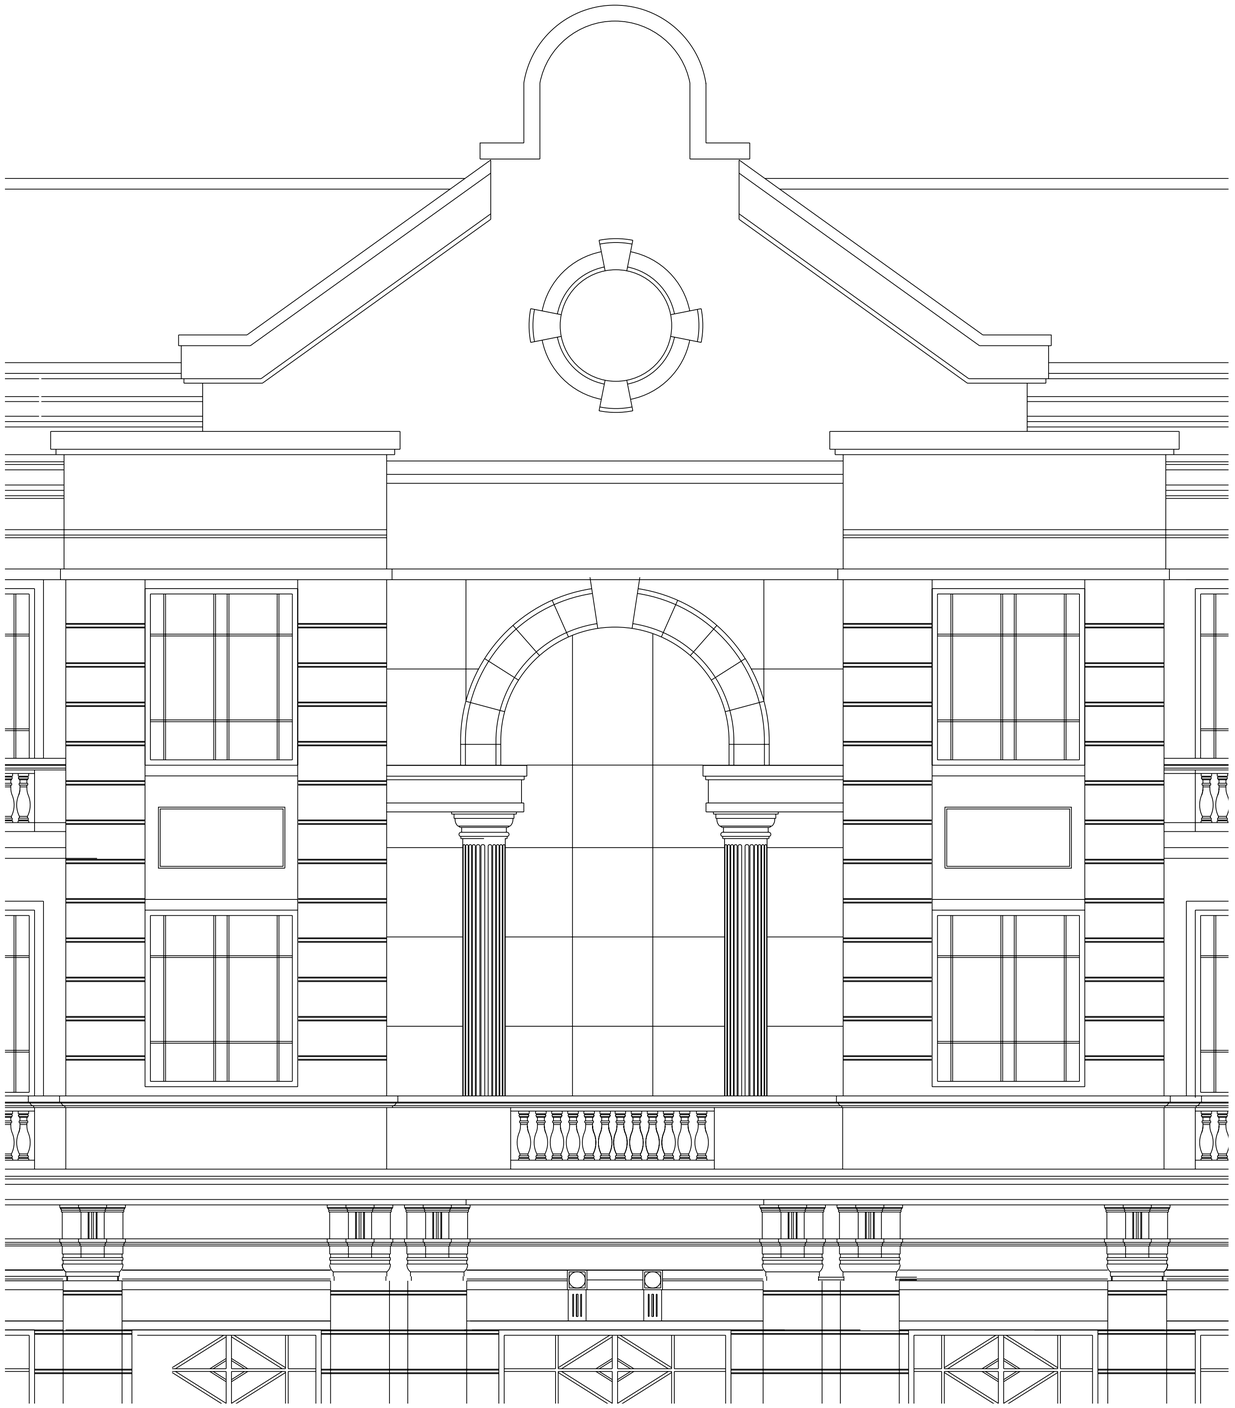

ORIGINAL: RECESSED CENTRE / PROJECTING PIERS

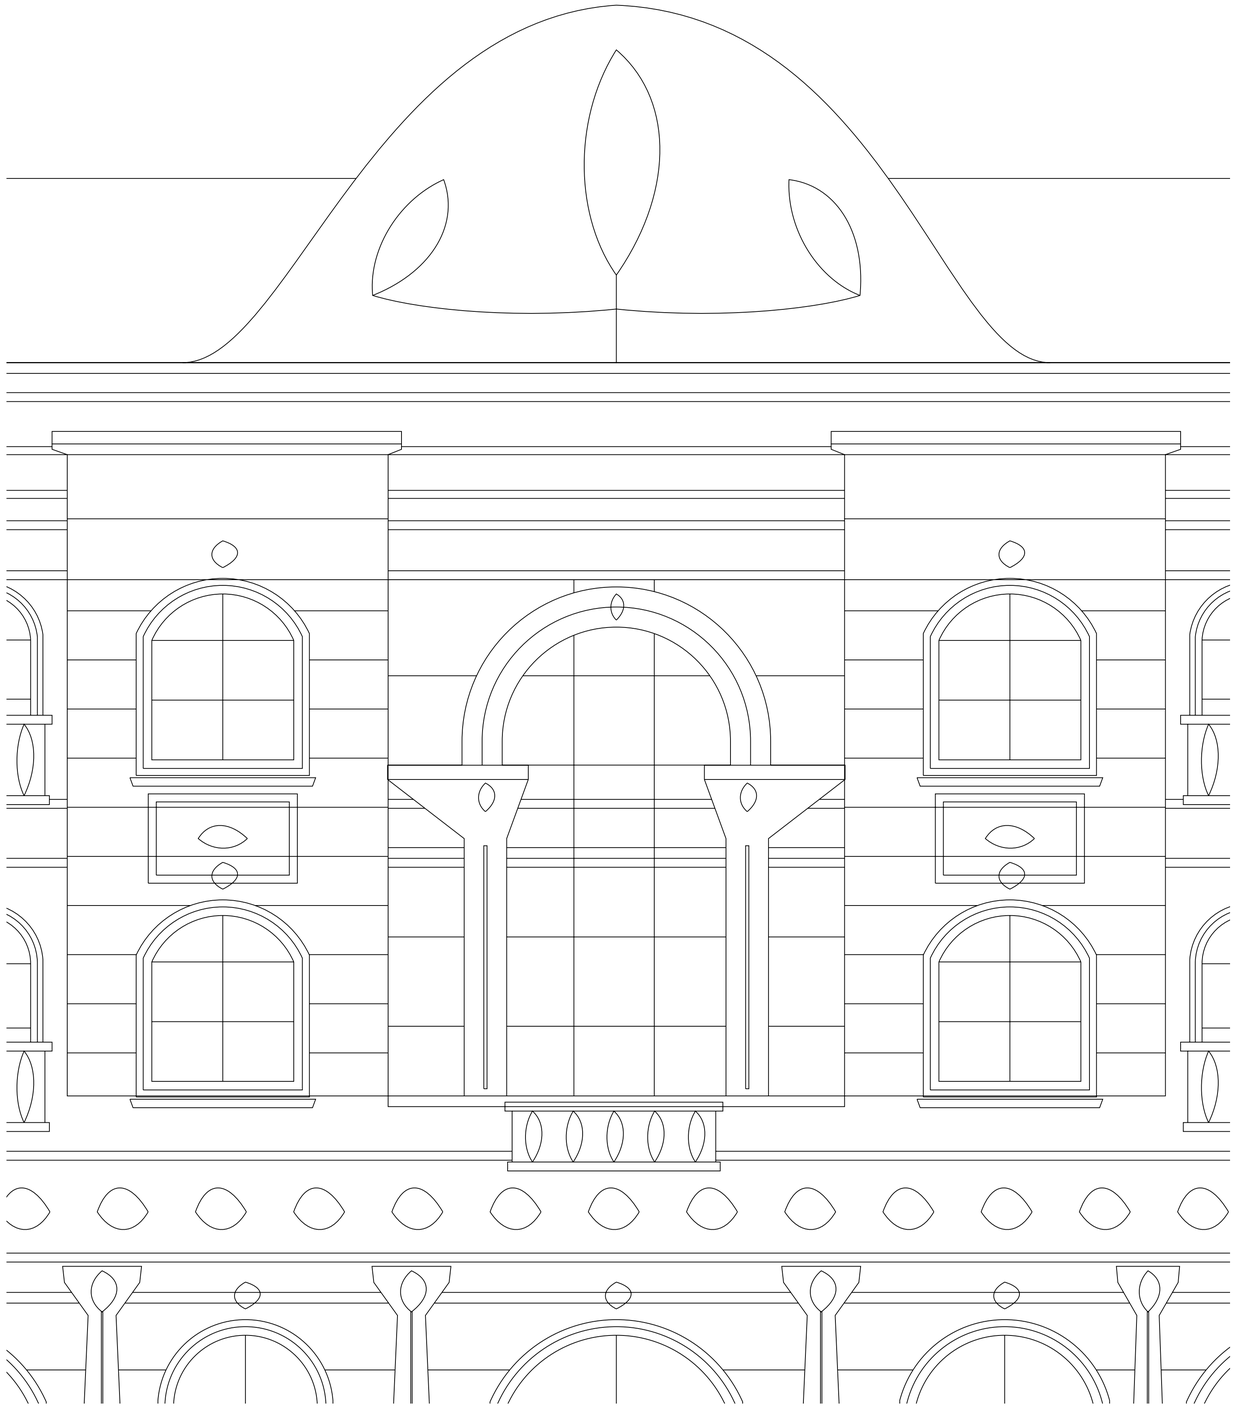

REVISED: SAME STRUCTURAL HIERARCHY / ART NOUVEAU DETAILS